

INSTITUTO PIAGET

BAIRRO DAS FLORES, VILA NOVA DE SANTO ANDRÉ - SANTIAGO DO CACÉM

OPERAÇÃO DE LOTEAMENTO

MEMÓRIA DESCRITIVA E JUSTIFICATIVA

Novembro de 2017

1. Introdução

A presente Memória Descritiva e Justificativa refere-se ao projecto de uma Operação de Loteamento que o Instituto Piaget pretende aprovar e levar a efeito num terreno do qual é superficiário, sito em Vila Nova de Santo André, concelho de Santiago de Cacém, inscrito no Artigo Matricial n.º 7004 e descrito na CRP sob o n.º 3617/20010130, com uma área total de intervenção de 181.182,57m^2.

2. Descrição e Justificação da solução proposta para a operação de loteamento

O referido terreno de que o Instituto Piaget é superficiário, situa-se na ZIL de Vila Nova de Santo André e é delimitado pela Rua das Camarinhas e Avenida Manuel da Fonseca.

A área total dessa parcela de terreno constitui a Área de Intervenção deste projecto de Loteamento Urbano.

O presente projecto de Loteamento prevê a constituição de 3 lotes, numerados de 1 a 3, todos destinados a actividades de interesse público, como a seguir se descrevem:

Lote 1 – com a área de 38.138,00m, uma área de implantação de 5.782,40m^2 e uma área bruta de construção de 9.750,00m^2, destina-se à implementação de um equipamento na área da saúde, com vista a apoiar toda a região do litoral Alentejano, e confronta a norte com a Rua das Camarinhas, a sul e nascente com zona verde (área de cedência), e a poente com a Avenida Manuel da Fonseca.

Lote 2 – com a área de 28.070,00m^2, uma área de implantação de 4.120,00m^2 e uma área bruta de construção de 5.000,00m^2, destina-se a uma zona de apoio a todo o conjunto, com vários edifícios destinados a Armazéns e Serviços existindo neste momento 2 armazéns já construídos e licenciados, e confronta a norte e nascente com o Lote 3, a sul com o novo arruamento público previsto, e a poente com a Avenida Manuel da Fonseca.

Lote 3 – com a área de 89.494,00m^2, uma área de implantação de 10.750,00m^2 e uma área bruta de construção de 16.050,00m^2, prevê a instalação de vários

edifícios, destinados a Serviços, Indústria (compatível com a função habitacional), Equipamentos e Armazém, e confronta a norte com a Rua das Camarinhas e zona verde (área de cedência), a sul com o Lote 2 e com o novo arruamento público previsto, a nascente com novo arruamento público previsto e a poente com a Avenida Manuel da Fonseca. Este lote será a reverter à Câmara Municipal de Santiago do Cacém.

Todos os lotes terão acesso independente a partir das vias públicas e serão servidos por lugares, ou parques de estacionamento, de acordo com a regulamentação em vigor.

3. Enquadramento da pretensão nos Planos Municipais e especiais de Ordenamento do Território existentes

A Área de Intervenção deste Projecto de Loteamento Urbano apenas é abrangida pelo "PDM – Plano Director Municipal" do concelho de Santiago do Cacém, visto não existir qualquer outro instrumento de Ordenamento do Território local, nomeadamente para a área geográfica de Vila Nova de Santo André.

A proposta deste projecto respeita em absoluto as prescrições da Planta de Ordenamento e do regulamento do referido Plano Director Municipal, assim como restante legislação aplicável.

4. Integração urbana e paisagística da operação

A operação de loteamento, juntamente com as edificações a projectar e construir ao seu abrigo neste sector sudeste de Vila Nova de Santo André, constituirão uma importante mais-valia para o local, para a cidade, para o concelho de Santiago de Cacém e para esta região do litoral Alentejano.

As construções previstas terão volumetria e imagem semelhantes às dos edifícios já construídos pelo Instituto Piaget, pelo que consideramos que vai haver uma perfeita

integração urbana e paisagística desses novos imóveis, o que será ainda valorizado pelas amplas zonas verdes a criar.

5. Número de lotes e respectivas áreas e áreas de implantação dos edifícios

Este Projecto de Loteamento Urbano sustentará o desenvolvimento de uma importante área de equipamentos nas áreas da Educação, Turismo e Saúde promovida pelo Instituto Piaget.

Desse conjunto de equipamentos alguns já existem em terrenos confinantes com o loteamento proposto, caso do "ISEIT", uma Escola de Ensino Superior Universitário, o "Hotel VilaPark", uma importante e confortável unidade hoteleira, e dois armazéns de apoio.

O terreno será repartido por 3 lotes, com áreas e características adaptadas à sua finalidade, conforme o seguinte Quadro Sinóptico:

QUADRO SINÓPTICO

n.º Lote	**Área do Lote** (m^2)	**Área de Implantação** (m^2)	**n.º Pisos**	**Área Bruta Construção** (m^2)	**Volume Construção** (m^3)	**Tipologia Ocupação**
1	38.138,00	5.782,40	2	9.750,00	57.824,00	Serviços/ Equipamento
2	28.070,00	4.120,00	2	5.000,00	41.200,00	Serviços/Armazém
3	89.494,00	10.750,00	2	16.050,00	107.500,00	Serviços/Indústria/ Equipamento/ Armazém

6. Área de construção e volumetria dos edifícios com indicação dos Índices Urbanísticos adoptados

N.º Lote	**Área do Lote** (m^2)	**Área de Implantação** (m^2)	**Área Bruta de Construção** (m^2)	**Índice de Implantação**	**Índice de Construção**
1	38.138,00	5.782,40	9.750,00	0,151	0,255
2	28.070,00	4.120,00	5.000,00	0,146	0,178
3	89.494,00	10.750,00	16.050,00	0,120	0,179

7. Cércea e número de pisos acima e abaixo da cota de soleira de cada edifício

Os edifícios existentes, projectados e previstos, terão um máximo de 2 pisos, rés-do-chão e 1º andar. Poderá recorrer-se a soluções de duplo pé-direito, caso as necessidades de funcionamento da actividade a desenvolver o justifiquem. Propõe-se uma altura máxima de edificação de 10,00m que pode ser diferente caso seja tecnicamente e construtivamente justificada a impossibilidade de cumprimento desse valor máximo. Se se verificar necessário para cumprimento da Portaria n.º 216-B/2008 de 3 de Março ou por motivos de instalação de áreas técnicas específicas, poderá ser permitida a construção de cave enterrada, desde que não seja extrapolado o polígono máximo de implantação definido em Planta Síntese de loteamento.

8. Áreas destinadas a Espaços de Utilização Colectiva, incluindo Espaços Verdes

No que concerne às áreas de verde urbano e espaços de equipamentos de utilização colectiva, deverão ser observados os parâmetros definidos na Portaria n.º 216-B/2008 de 3 de Março:

Parâmetros de dimensionamento

Serviços	28 m^2/100 m^2 a. c. serv.	25 m^2/100 m^2 a. c. serv.	3 lugares/100 m^2 a. c. serv. para establ. ≤ 500 m^2. 5 lugares/100 m^2 a. c. serv. para establ. > 500 m^2. O número total de lugares resultante da aplicação dos critérios anteriores é acrescido de 30 % para estacionamento público.
Indústria e ou armazéns	23 m^2/100 m^2 a. c. ind./ armaz.	10 m^2/100 m^2 a. c. ind./ armaz.	1 lugar/75 m^2 a. c. ind./armaz. Pesados: 1 lugar/500 m^2 a. c. ind./armaz., com um mínimo de 1 lugar/lote (a localizar no interior do lote). O número total de lugares resultante da aplicação dos critérios anteriores é acrescido de 20 % para estacionamento público.

Todo este projecto assenta num princípio de valorização dos espaços e dos equipamentos de utilização colectiva, pelo que, no que se refere a estes espaços, propõe-se a definição de uma única área que engloba ambos os usos, devendo manter-se o terreno natural, por forma a integrar e valorizar o alto valor ecológico do meio ambiente no local; esta é mesmo uma das grandes qualidades do projecto.

O espaço reservado para esse fim encontra-se identificado nas peças desenhadas que integram o Loteamento e cumpre com os parâmetros definidos na parametrização acima referida.

Não está prevista nenhuma edificação de carácter habitacional, apenas construções e espaços destinados a actividades culturais, de lazer e de conforto.

Há também a registar que uma parte maioritária dos equipamentos propostos ficarão abertos à utilização colectiva, quer no âmbito do lazer, quer – de forma mais restrita e direccionada – no âmbito da saúde.

9. Numero de estacionamentos necessários

n.º Lote	Área do Lote (m^2)	Uso	Área Implantação (m^2)	n.º Pisos	Área Bruta Construção (m^2)	Volumetria (m^3)	Lugares Estacionamento
1	38.138,00	Serviços/ Equipamento	5.782,40	2	9.750,00	57.824,00	426
2	28.070,00	Serviços/Armazém	4.120,00	2	5.000,00	41.200,00	142
3	89.494,00	Serviços/Indústria/ Equipamento/ Armazém	10.750,00	2	16.050,00	107.500,00	486

Os cálculos para verificação do número de estacionamentos necessários foram efectuados de acordo com o estipulado na Portaria nº 216-B/2008 de 3 de Março. No que respeita aos estacionamentos necessários ao lote 2, e uma vez que alguns edifícios se encontram já construídos, os cálculos foram efectuados tendo em conta as áreas e usos específicos desses edifícios, somando a previsão dos necessários para uma nova unidade a construir.

No que se refere aos lotes 1 e 3, uma vez que são permitidos vários usos mas não há já a definição exacta de qual deles vai ser predominante, com o sentido de encontrar uma solução equilibrada e justa em termos de ocupação de solo, os cálculos executados foram feitos sobre uma base de que a área de construção máxima permitida será distribuída proporcionalmente por cada uso proposto para lote.

No entanto, em sede de licenciamento do edifício estes valores poderão ser adaptados, desde que seja dado cumprimento ao definido na Portaria n.º 216-B/2008 de 3 de Março.

De acordo com a parametrização acima referida, serão necessários prever 819 lugares de estacionamentos, aos quais acrescerão 228 estacionamentos públicos e 28 lugares para estacionamento de veículos pesados. Verifica-se que é possível dar cumprimento a estas necessidades de estacionamento dentro da área loteada.

10. Generalidades do projecto de arquitectura

O projecto é livre em solução construtiva, linguagem, cromatismo, etc., devendo no entanto enquadrar-se com o tipo de arquitectura observada na envolvente próxima.

A implantação dos edifícios nos Lotes deve respeitar os polígonos máximos de implantação propostos em Planta Síntese.

A volumetria deve respeitar a prevista na Planta Síntese e nos quadros Urbanimétricos, ou seja, 2 pisos. Poderá ser permitida a construção de cave enterrada para estacionamentos ou zonas técnicas, desde que não extrapolem os polígonos máximos de implantação.

11. Condicionamentos relativos à implantação de edifícios e construções anexas

Os condicionamentos relativos à implantação das edificações previstas são os prescritos pela Legislação e Regulamentação (geral e municipal) em vigor e pelo Regulamento do Plano Director Municipal do concelho de Santiago do Cacém.

As implantações definidas neste projecto de loteamento, e respectivas áreas, correspondem aos máximos que se poderão utilizar nos projectos a elaborar para o local e respectivas construções.

12. Solução adoptada para o funcionamento das Redes de Abastecimento de Água, Energia Eléctrica, Saneamento, Gás e Telecomunicações e suas ligações às redes gerais

12.1 Rede de Abastecimento de Água

12.1.1 - Constituição do Sistema

O projecto de loteamento será concebido por dois sistemas distintos, um de distribuição para consumo ao domicílio e zonas de equipamentos e outro de rega para zonas verdes.

12.1.2- Rede de distribuição de água para consumo

A rede para consumo será independente para cada lote e será alimentada diretamente da rede pública.

O estudo apresentado carece ainda de confirmação da pressão disponível na rede e apreciação da solução proposta às Águas de Santo André. Caso se julgue necessário, será previsto um reservatório a localizar estrategicamente que vise assegurar, quer as pressões mínimas exigidas para cada lote, quer uma reserva de combate a incêndio.

12.1.3 - Rede de Rega

A solução a adoptar na rede de rega e perante a percentagem elevada de áreas verdes será global para o loteamento. A captação de água directa do solo, caso os estudos venham a revelar viabilidade e sustentabilidade ao sistema, é do ponto de vista económico a solução mais aceitável, garantido simultaneamente economia de custos ao promotor e excesso sobrecarga de consumo da rede em alta.

12.2 Rede de Drenagem de Águas Residuais Domésticas e Pluviais

12.2.1 Generalidades

O presente estudo inclui a drenagem das águas residuais produzidas dos lotes definidos na operação de loteamento, a qual foi condicionada pela divisão dos lotes e a obrigatoriedade dos efluentes drenarem para os arruamentos públicos.

12.2.2 - Rede de Drenagem de Águas Residuais Domésticas

Observando a topografia do terreno verifica-se a possibilidade de se implementar uma central elevatória que servirá os lotes 1,2 e 3. Os efluentes destes lotes serão gravíticos para um colector principal a localizar na Rua das Camarinhas. O destino final destes efluentes será a câmara de ligação do sistema de intercepção de águas residuais comunitárias domésticas, onde será localizada a estação elevatória.

Estas soluções carecem de aprovação dos serviços competentes e poderão ser alteradas mediante análise de uma outra alternativa, que se venha a verificar-se economicamente e tecnicamente mais vantajosa.

12.2.3 - Rede de Drenagem de Águas Pluviais

Em analogia ao sistema implementado da rede de drenagem de águas residuais domésticas, os lotes 1,2 e 3 serão drenados a uma central elevatória antes da sua intercepção no colector público situado na Rua das Camarinhas.

12.3 Infraestruturas de Eletricidade

12.3.1 - Introdução

O seguinte estudo é relativo à operação de infra-estruturas de electricidade de um Loteamento, sendo o requerente o Instituto Piaget.

3.2 Âmbito do Projecto

Das instalações eléctricas a executar no âmbito do presente projecto, indica-se sem carácter exaustivo, as seguintes:

- Redes de distribuição incluindo:
    - cabos de alimentação;
    - rede de tubagem;
- Iluminação exterior pública.

12.3.3 - Observações

As diversas instalações eléctricas serão concebidas de harmonia com:

Regras Técnicas das Instalações Eléctricas de Baixa Tensão

Regulamento de Segurança de Subestações e Postos de Transformação e de Recepção e Corte

Regulamento de Segurança de Redes de Distribuição de Energia Eléctrica em Baixa Tensão".

12.3.4 - Concepção das Instalações de MT

A alimentação de energia eléctrica a cada um dos lotes será em Média Tensão

Em virtude das potências previsíveis de alimentação a cada edifício, optou-se por postos de transformação e seccionamento dedicados a cada um dos lotes.

Os Postos de Seccionamento e Transformação (PST) serão instalados num edifício monobloco de manobra interior, com todos os elementos para Posto de Seccionamento e Transformação de Distribuição

Os PST deverão ser acessíveis através da via pública por equipas do distribuidor de energia local.

As canalizações eléctricas destinadas aos PST, são estabelecidas do interior de tubos enterrados directamente no solo, no interior de valas com as características regulamentadas.

Estas valas serão abertas ao longo dos passeios e bermas dos arruamentos do espaço contemplado no espaço a intervencionar. Nas zonas de travessia de arruamentos, serão deixados tubos em espera para posterior enfiamento de cabos eléctricos, com acessibilidade garantida a partir de câmaras de visita.

Os tubos utilizados nas canalizações enterradas e nas travessias de arruamentos serão do tipo PEAD, com diâmetro de 125mm na rede de distribuição e 63mm na iluminação pública. Em cada travessia, para além dos tubos necessários para proteger os cabos previstos no projecto, deverão ser instalados 2 tubos de 125mm com efeito de reserva.

Iluminação Pública

A iluminação exterior dos arruamentos e vias a implementar no presente estudo é constituída por diversos tipos de aparelhos de iluminação, escolhidos em função do local ou zona a tratar e dos requisitos luminotécnicos usuais neste tipo de instalação.

12.3.5 - Conceção das Instalações de Iluminação

A iluminação de arruamentos é obtida através de luminárias instaladas em colunas metálicas com altura útil e interdistâncias entre colunas definidas em função das soluções encontradas.

O comando dos circuitos pertencentes à rede de iluminação exterior, será realizado por intermédio de interruptor crepuscular intercalado.

12.3.6 – Cálculos

Na falta de elementos relativos às potências previstas para o funcionamento dos edifícios a construir, optou-se pelas potências indicadas no quadro seguinte. Estas potências poderão sofrer alterações mediante a apresentação de novos dados relevantes para o projeto elétrico.

n.º Lote	Área do Lote (m²)	Uso	Área Implantação (m²)	n.º Pisos	Área Bruta Construção (m²)	Volumetria (m³)	Potência Previsível a Instalar
1	38.138,00	Serviços/ Equipamento	5.782,40	2	9.750,00	57.824,00	250
POTÊNCIA TOTAL DO POSTO DE TRANSFORMAÇÃO (KVA)							**250**
2	28.070,00	Serviços/Armazém	1 530.40	2	2 194.37	15 304.00	100
		Armazém	1 841.63	1	1 841.63	18 416.30	100
		Armazém	745,11	1/2	964.00	7 451.10	50
POTÊNCIA TOTAL DO POSTO DE TRANSFORMAÇÃO (KVA)							**250**
3	89.494,00	Serviços/Indústria/ Equipamento/ Armazém	10.750,00	2	16.050,00	107.500,00	400
POTÊNCIA TOTAL DO POSTO DE TRANSFORMAÇÃO (KVA)							**400**

12.4. Infraestruturas De Telecomunicações

O seguinte estudo é relativo à operação de infra-estruturas de telecomunicações de um Loteamento, sendo o requerente o Instituto Piaget

12.4.1 - Conceção das Instalações

A ligação das infraestruturas telefónicas do loteamento em estudo à rede de distribuição pública será assegurada por uma rede de condutas, onde, e em data oportuna, serão colocados os cabos de alimentação dos prédios

12.4.2 - Rede de Tubagens

Serão previstas, condutas a quatro furos, para tubagem em vala, ficando os tubos colocados ao longo dos passeios, envolvidos por terra cirandada ou por areia.

Os traçados das condutas deverão ser constituídos por troços rectilíneos, admitindo-se curvaturas até 2 cm/m.

Por regra a parte superior do bloco de condutas deverá ficar a uma profundidade mínima de 0,80 m. Nas travessias de arruamentos esta profundidade deverá ser superior a 1,00 m, sendo os tubos envolvidos por massa de cimento.

Em frente a cada imóvel serão estabelecidas caixas do tipo NR2 de onde sairão quatro tubos de PVC de 90 mm de diâmetro para futura entrada subterrânea de cada lote.

Nas travessias e cruzamentos serão estabelecidas caixas do tipo NR3

12.4.3 - Construção das Câmaras

As câmaras serão paralelepipédicas, construídas no local ou pré-fabricadas em betão armado. Deverão possuir as seguintes dimensões interiores (respectivamente comprimento, largura e altura):

- NR2 – 0,75x1,20x1,50 m
- NR3 – 0,75x1,50x1,50 m

O fundo das câmaras poderá ser constituído de cascalho com 0,15 m de espessura, coberto de massame de betão ao traço 1:4:5. As paredes serão executadas com tijolo burro ou blocos de cimento assentes ao traço 1:3 (1 volume de cimento e 3 de areia). O reboco será executado com argamassa ao traço 1:3 com uma espessura de 2 cm.

12.4.4 - Dimensionamento da REDE

Na falta de elementos relativos às necessidades dos edifícios a construir, optou-se pelo seguinte dimensionamento dos lotes. Este dimensionamento poderá sofrer alterações mediante a apresentação de novos dados relevantes para o projecto de telecomunicações.

13. Estrutura Viária adoptada, especificando as áreas previstas para vias, acessos e lugares de estacionamento de veículos

A estrutura viária do projecto assenta nas vias existentes, uma estrutura consolidada no tecido urbano de Vila Nova de Santo André que foi respeitada e integrada.

No que se refere à relação do número de lugares de estacionamento com a legislação específica (Portaria 216-B/2008 de 3 de Março) vimos esclarecer:

Lote 1 - pela referida legislação necessitaria de um total de 423 lugares de estacionamento (325 privados + 98 públicos), sendo possível garantir 426 lugares no interior do lote, ou seja, um excedente de 3 lugares. Dessa forma, verifica-se que é dado cumprimento à legislação aplicável.

Lote 2 - na actual versão deste projecto de loteamento são garantidos 140 lugares (111 privados + 29 públicos) e 8 lugares de estacionamento para veículos pesados, pelo que se cumpre a referida Portaria, excedendo-se até em 2 lugares os necessários.

Lote 3 - de acordo com as áreas de construção e os usos permitidos, serão necessários garantir 486 lugares para ligeiros (384 privados + 102 públicos) e 20 lugares para pesados. Dada a dimensão e configuração do lote 3 é possível garantir-se dentro do lote os estacionamentos necessários, dando-se cumprimento à legislação aplicável.

Ao longo do novo arruamento que se prevê vir a ser projetado, são ainda garantidos cerca de 114 lugares de estacionamento público, dentro da área de intervenção

De referir ainda que, em fase de licenciamento dos diversos edifícios os valores atrás mencionados poderão ser adaptados, desde que seja dado cumprimento ao definido na Portaria n.º 216-B/2008 de 3 de Março.

14. Índice das Peças Desenhadas

01 – Levantamento Topográfico ……..…….…… esc. 1:1000

02 – Planta da Situação Existente ……..…… esc. 1:1000

03 – Planta de Síntese ……..…….…… esc. 1:1000

03a – Planta de Síntese com indicação das redes de Abastecimento de Água e de Saneamento, Energia Eléctrica, Gás e Inf. de Telecomunicações ……..…… esc. 1:1000

04 – Planta das Áreas de Cedência ……..…..… esc. 1:1000

05 – Plano de Acessibilidades ……..…….. esc. 1:1000

15. Plano de Acessibilidades


Refere-se este ponto ao Plano de Acessibilidades, elaborado de acordo com o definido em Decreto-Lei n.º 163/2006 de 8 de Agosto, constante das peças desenhadas (Desenho 05) do projecto.

Com base no DL acima referido, as áreas do loteamento serão dotadas de uma rede de percursos pedonais, livre de quaisquer obstáculos, contínua e coerente, que proporcione o acesso seguro e confortável das pessoas com mobilidade condicionada a todos os pontos relevantes da sua estrutura activa, nomeadamente:

- passeios públicos, cuja a largura mínima será de 1,60m (entre o muro de limite dos lotes e os candeeiros de iluminação pública)
- espaços públicos de recreio e lazer
- equipamentos colectivos
- passadeiras (procurou-se definir um numero suficiente de passadeiras para garantir o menor percurso entre as mesmas. Para além do rebaixamento dos passeios de ambos os lados da passadeira, será assegurada uma boa legibilidade do espaço através da adopção de elementos e texturas de pavimentos que forneçam, nomeadamente a pessoas com deficiência da visão, a indicação dos principais percursos de atravessamento e garantam a sua a segurança)
- paragens de transportes públicos, caso venham a ser implementadas nos novos arruamentos
- espaços de estacionamentos de viaturas (a localização de estacionamento para pessoas com mobilidade condicionada, ao longo dos arruamentos,

privilegiará a proximidade às entradas dos edifícios e dos equipamentos no espaço público)

- contentores de resíduos sólidos urbanos.

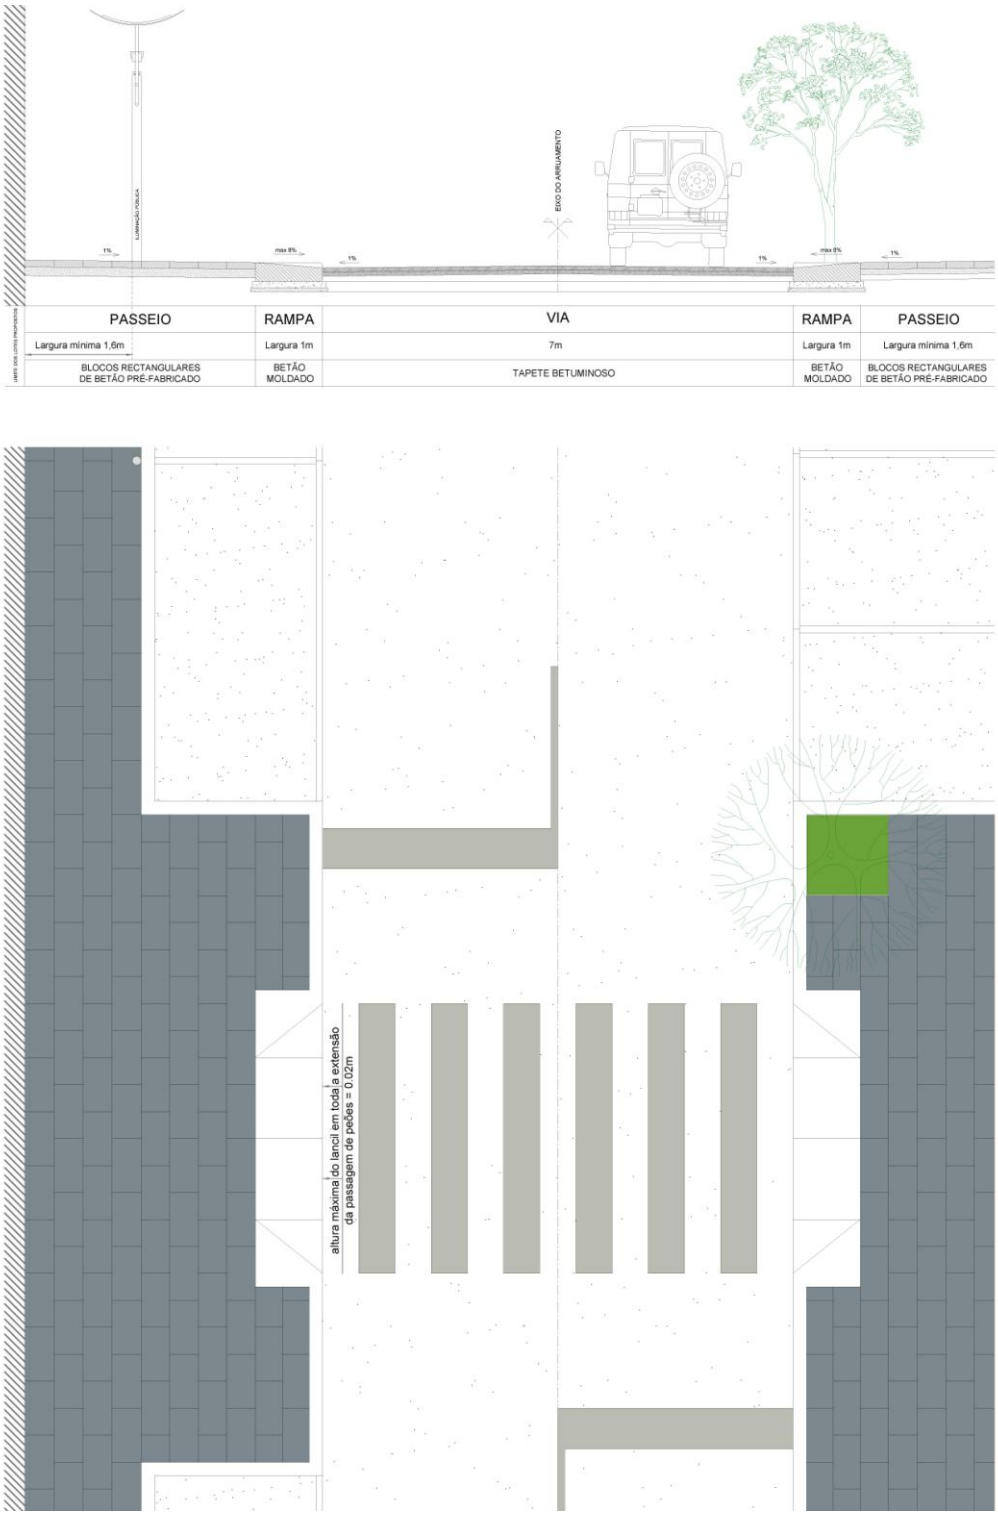

Perfil Tipo Proposto (s/escala)

16. Identificação dos Técnicos autores e do Coordenador dos Projectos

. Paula Marisa Valente Rocha, Arq. ..... Projecto da Operação de Loteamento

. Hugo Manuel Ferreira dos Santos, Eng. ..... Projecto das Redes e Coordenador dos Projectos

. Joel Filipe Ascenso Faria da Silva, Eng. ..... Relatório do Estudo Acústico

Em tudo o omisso nesta Memória Descritiva e Justificativa, serão respeitadas as normas legais aplicáveis, nomeadamente o PDM, Decreto-Lei n.º 163/2006 de 08/08, Decreto-Lei n.º 555/99 de 16/12 na sua redacção actual, assim como restante legislação específica aplicável.

15 de Dezembro de 2017

Assinado por : **PAULA MARISA DE MATOS VALENTE CLEMENTE ROCHA**
Num. de Identificação Civil: BI092503373
Data: 2017.12.18 20:45:27 Hora padrão de GMT

CARTÃO DE CIDADÃO

Paula Marisa Valente Rocha
Arquitecta