MEMÓRIA DESCRITIVA E JUSTIFICATIVA

Refere-se a presente memória descritiva e justificativa à alteração ao Loteamento do Lameirinho, titulado pelo alvará n.º 6/2002, que a Câmara Municipal de Angra do Heroísmo pretende levar a efeito. A proposta visa a alteração do Lote 219, situado na zona Poente do Loteamento, Rua Ilha do Corvo, Bairro do Lameirinho, freguesia de Nossa Senhora da Conceição.

Contexto:

O limite do Lote 219 na altura da constituição do Loteamento foi incorretamente delimitado com uma área total de 5450 m2.

Atualmente de acordo com levantamento topográfico o Lote tem 5920 m2, os restantes 470 m2 ficaram integrados nos espaços verdes de utilização coletiva do loteamento, quando na realidade faziam parte do Lote 219.

Proposta de Alteração:

A proposta consiste na alteração do Lote 219 (5920 m2) em Lote 219 A com 2409 m2, Lote 220 com 2545 m2 e restante área para arruamentos públicos com 966 m2.

Na sequência da correção da área do Lote 219 existente, serão deduzidos 470 m2 dos espaços verdes e utilização coletiva.

A alteração proposta vai de encontro ao referido no Alvará do loteamento e de acordo com o quadro anexo à planta geral do loteamento, no qual refere a área do Lote 219 como “área para futura expansão ou equipamento”.

Tem a finalidade de integrar o novo arruamento “Rua Ilha do Corvo”, criando desta forma um novo acesso ao interior do Bairro, e a construção de um Equipamento - Centro Comunitário e Social no Lote 219A, tal como área para futura construção no Lote 220, desde que, sejam respeitadas as condições referidas no alvará de loteamento e os respetivos polígonos de implantação agora propostos.

Relativamente aos estacionamentos, de acordo com a Portaria n.º 216-B/2008, de 3 de Março, são necessários 34 estacionamentos para este equipamento, dos quais 8 são para estacionamento público.

Com o novo arruamento estão previstos 10 estacionamentos na via pública, os restantes deverão ficar acautelados no projeto de licenciamento do equipamento.

Neste sentido, propõe-se para o Lote 219A e Lote 220 as seguintes condições:

a) Índice máximo de utilização do solo: 1,0;

b) Número máximo de pisos: 2 mais aproveitamento de sótão e cave;

c) As construções deverão ser implantadas de acordo com os polígonos de implantação definidos nas peças desenhadas;

d) Número de estacionamentos, de acordo com Portaria n.º 216-B/2008, de 3 de Março.

Quadro Síntese das áreas totais existentes e áreas totais propostas

	Existente (m2)	Proposta (m2)
Lote 219	5 450	-
Lote 219 A	-	2409
Lote 220	-	2545
Espaços verdes	10 629,00	10 159,00
Arruamentos	21 342,29	22 308,29
TOTAL	82 888,00	82 888,00


O alteração de loteamento proposta cumpre com o Plano de Pormenor de Salvaguarda de Angra do Heroísmo.

A área em causa está classificada, de acordo com a planta de Implantação do PPSAH, como Espaços Urbanos a Consolidar – Áreas a Consolidar.

Todas as construções ou alterações devem cumprir com o Plano de Pormenor de Salvaguarda de Angra do Heroísmo.

Angra do Heroísmo, setembro de 2020

Pedro Candeias, Arquiteto

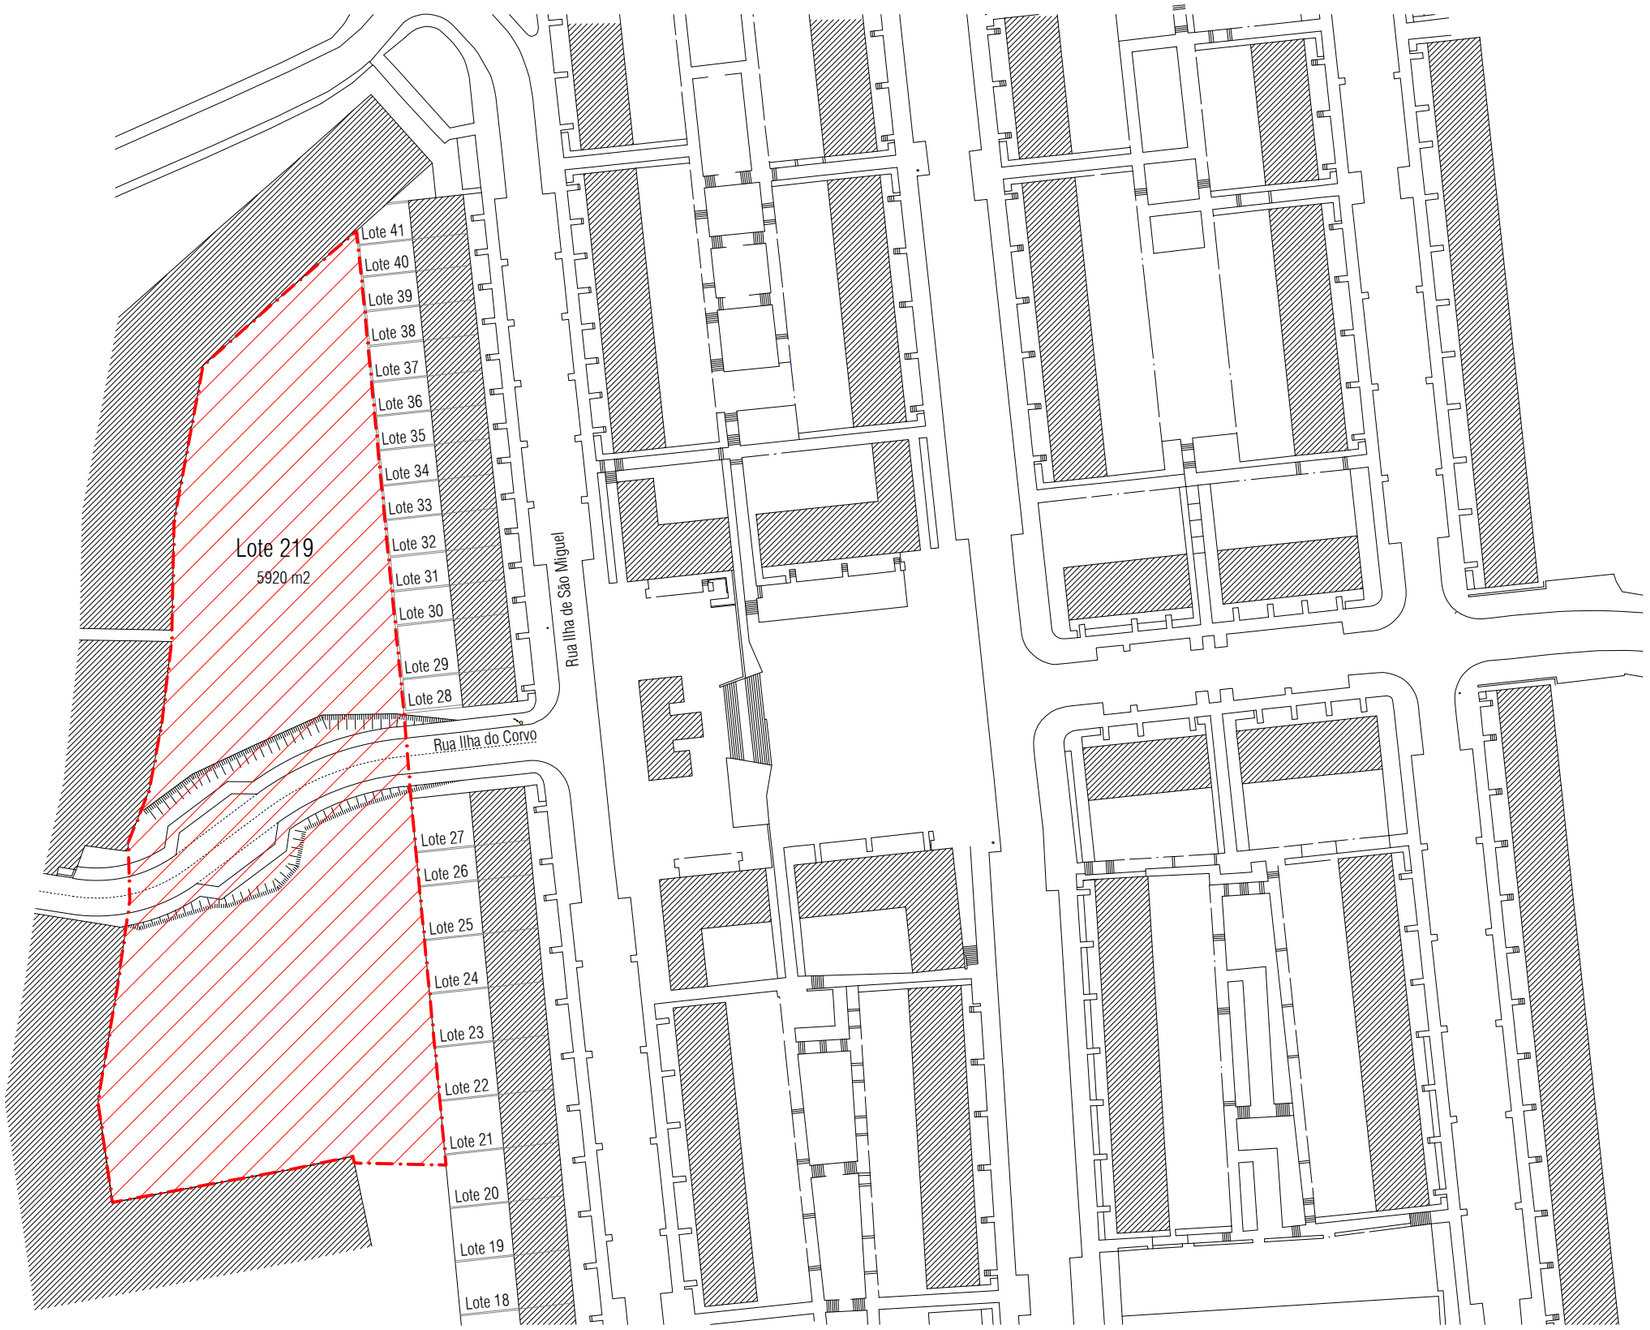

N

LEGENDA:

- Limite do Lote 219
- Edificações


CÂMARA MUNICIPAL DE ANGRA DO HEROÍSMO

Local	**Bairro do Lameirinho**
Freguesia	**Conceição**
Concelho	**Angra do Heroísmo**

PLANTA
Lote 219 Existente
Loteamento do Lameirinho

Escala: **1 : 1000**

Data:	Desenho:
Setembro 2020	**1**

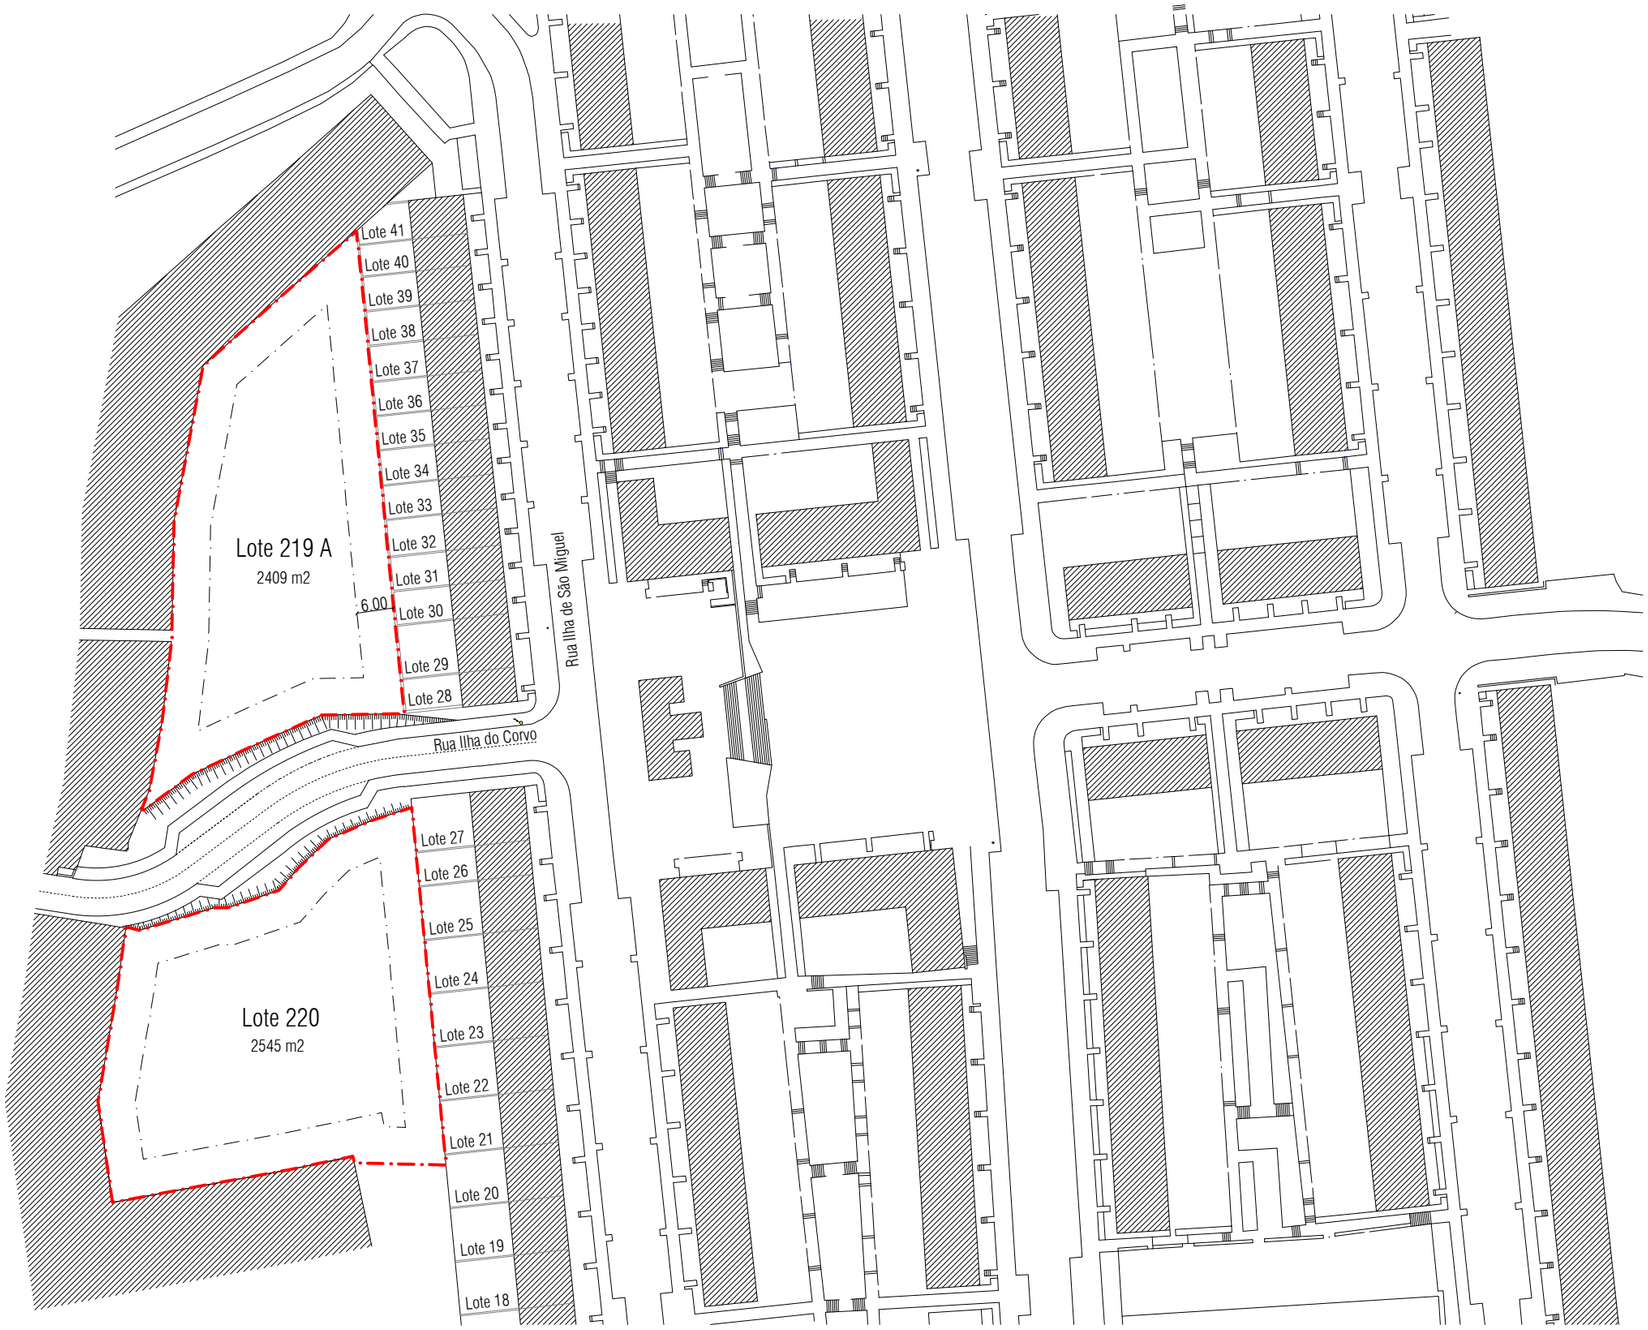

LEGENDA:

- Limite do Lote 219 A e Lote 220
- Polígono de Implantação
- Edificações

CÂMARA MUNICIPAL DE ANGRA DO HEROÍSMO

Local	**Bairro do Lameirinho**
Freguesia	**Conceição**
Concelho	**Angra do Heroísmo**

PLANTA
Proposta de alteração
Loteamento do Lameirinho

Escala: **1 : 1000**

Data: **Setembro 2020**

Desenho: **2**